

Property:
COFFMAN APTS
INDIANAPOLIS, INClient:
**COHEN MIZRAHI
PROPERTIES LLC**

SEAL:

SCALE: AS NOTED


DWG BY: R.M.

Drawing Title:
**PROPOSED
FLOOR PLANS**

Drawing Number:

A-100.00

01 of 05

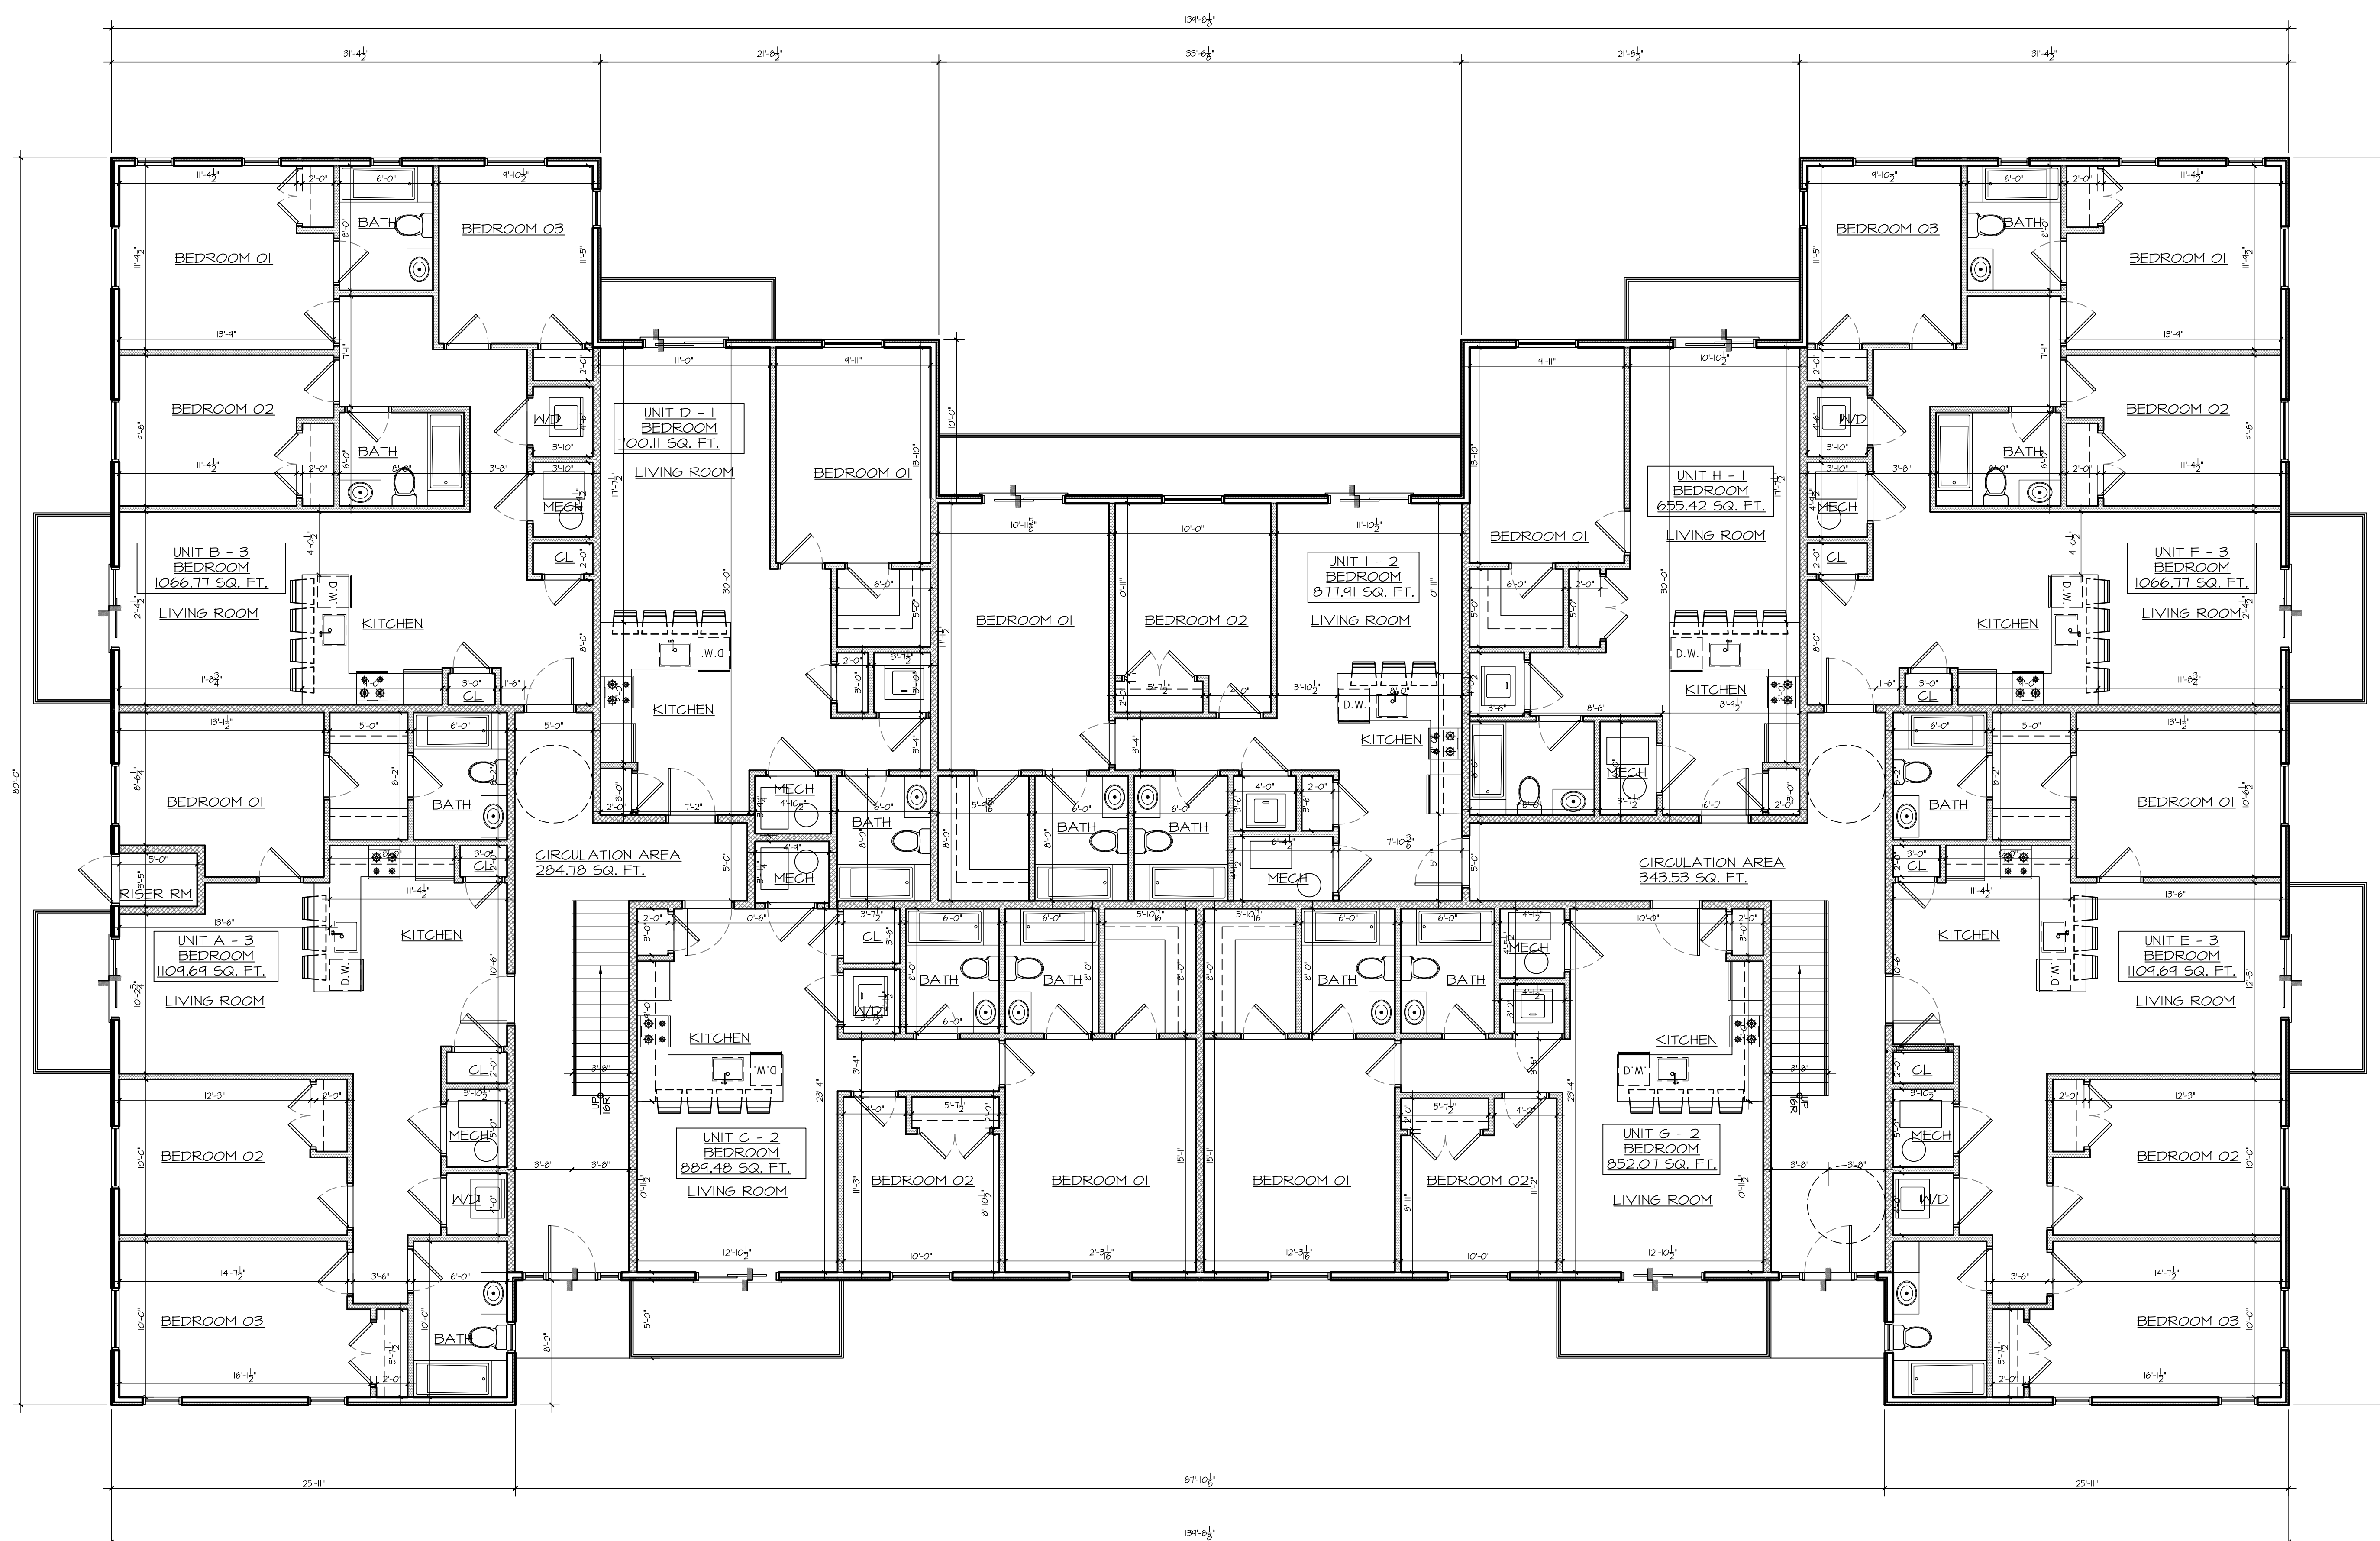

Property:
COFFMAN APTS
INDIANAPOLIS, IN

Client:
**COHEN MIZRAHI
PROPERTIES LLC**

SEAL:

SCALE: AS NOTED


DWG BY: R.M.


Drawing Title:
**PROPOSED
FLOOR PLANS**

Drawing Number:

A-101.00

02 of 05

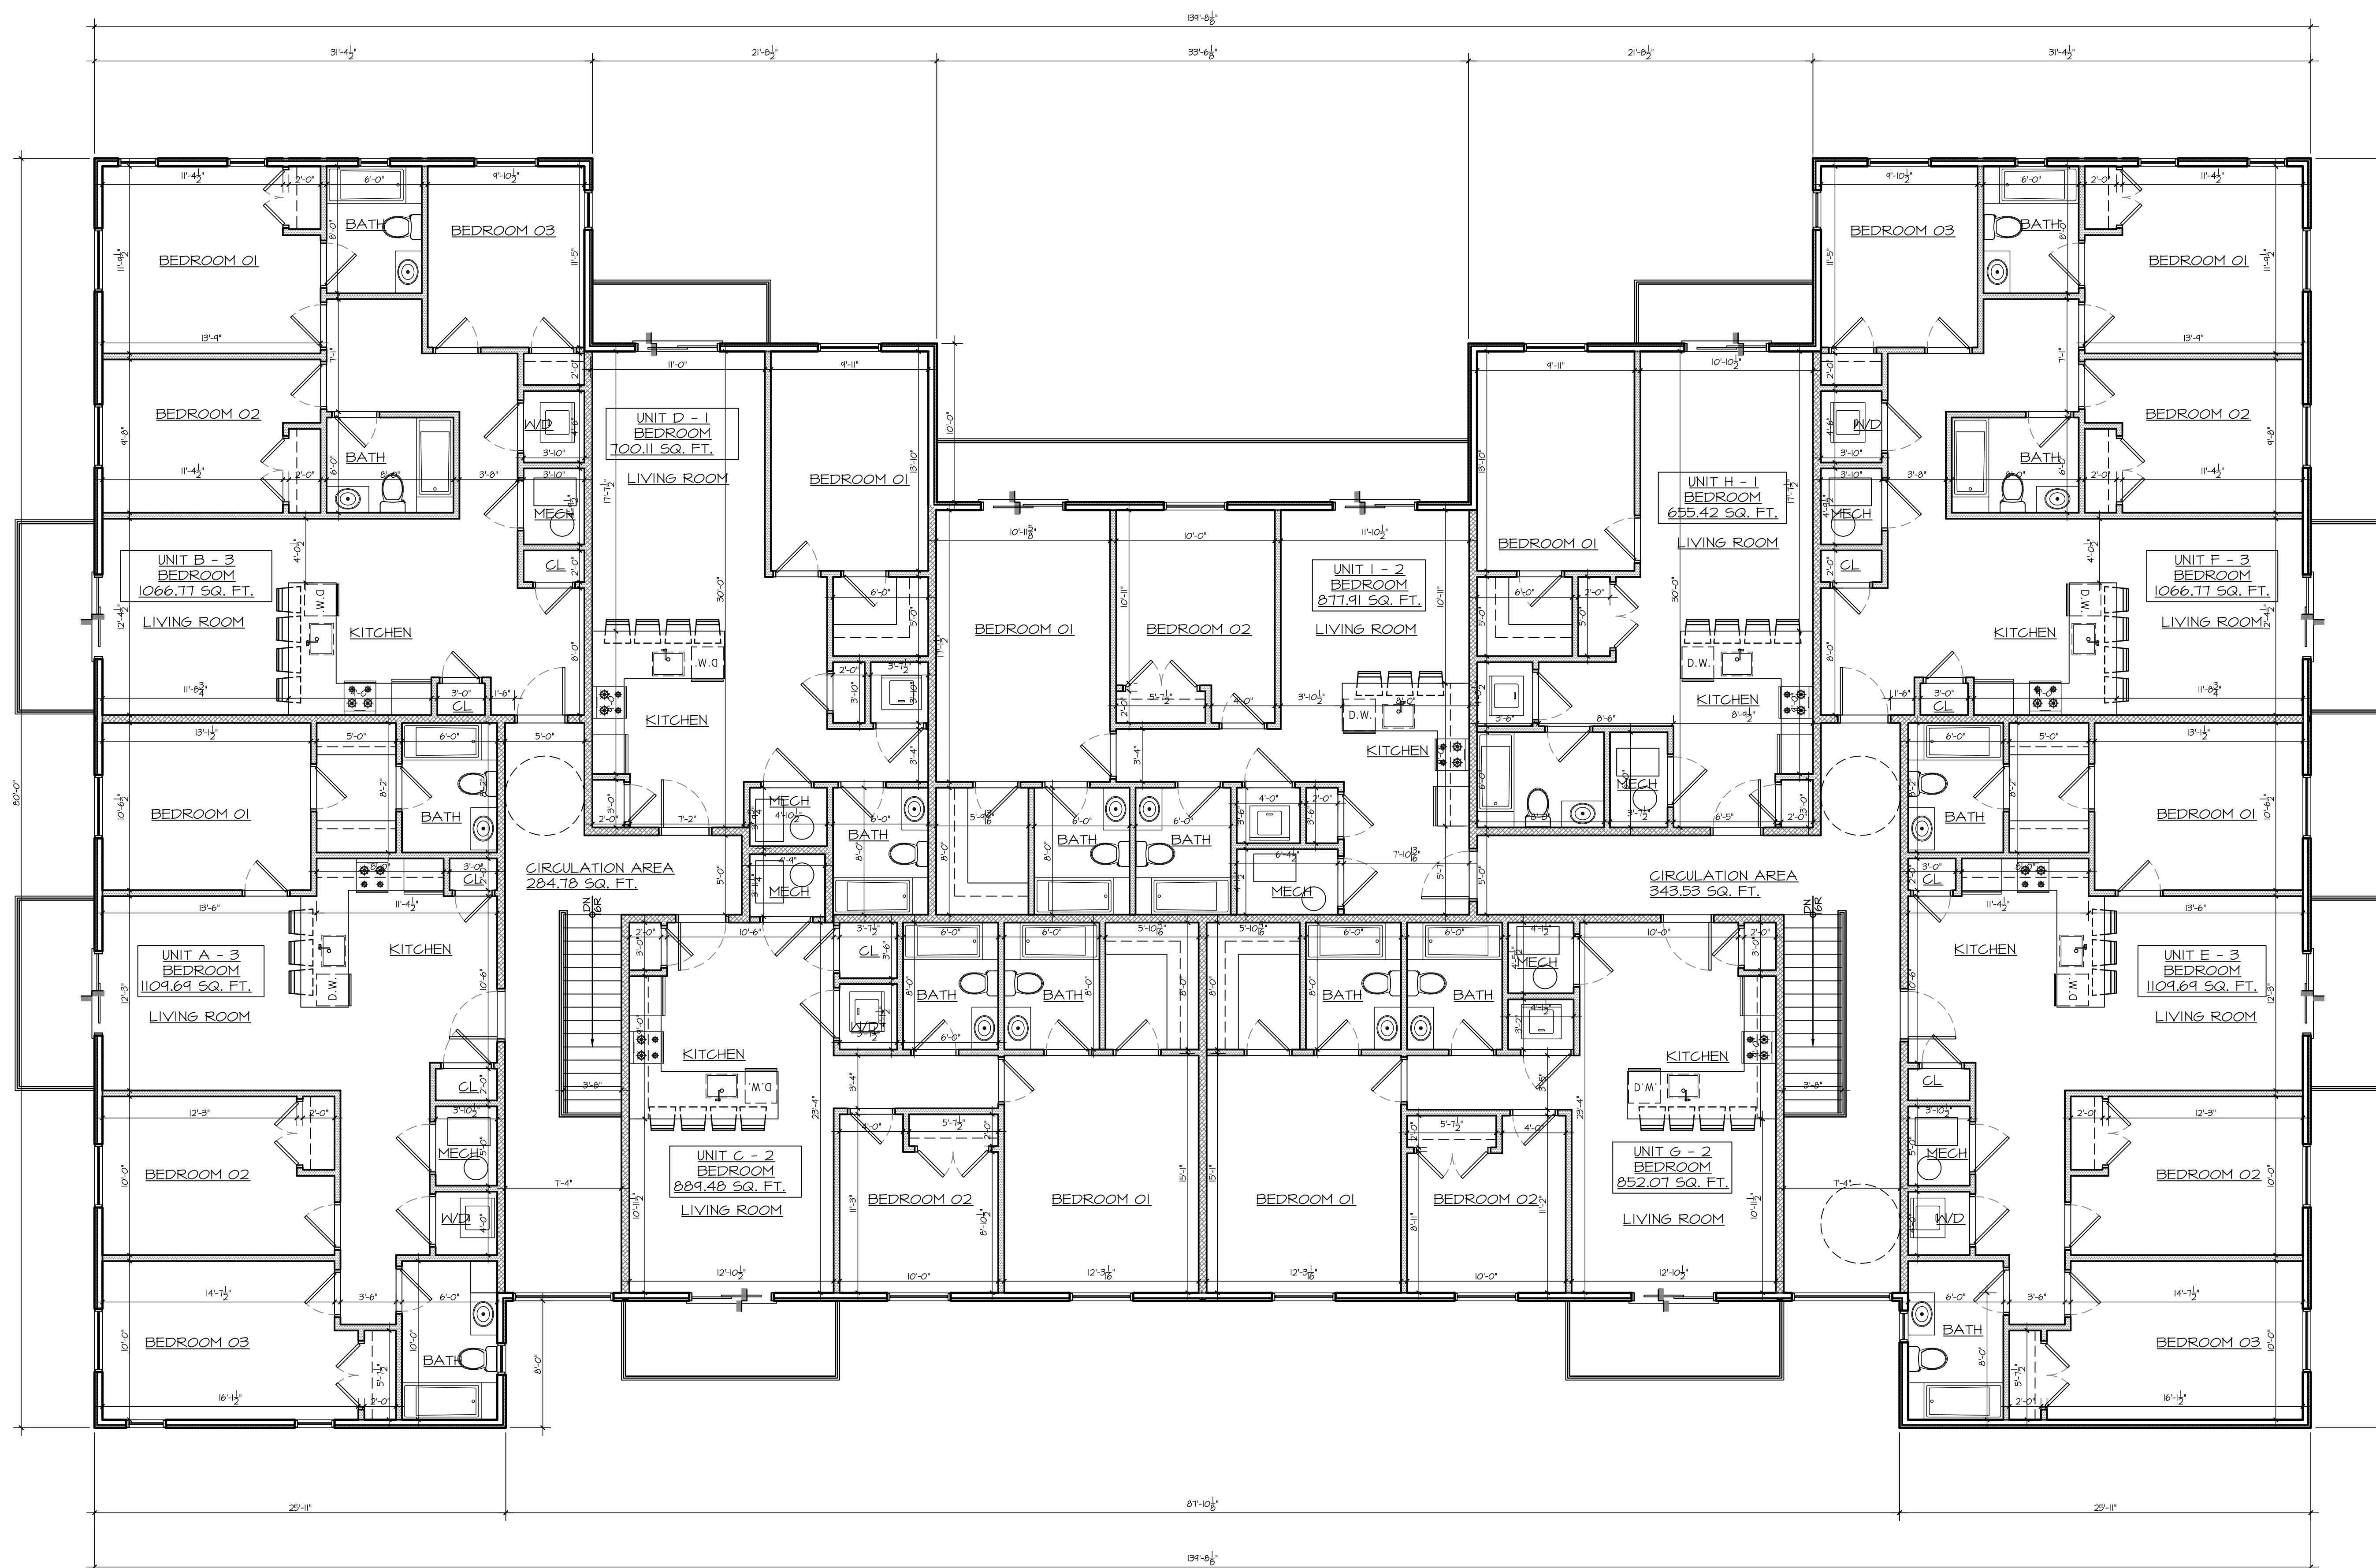

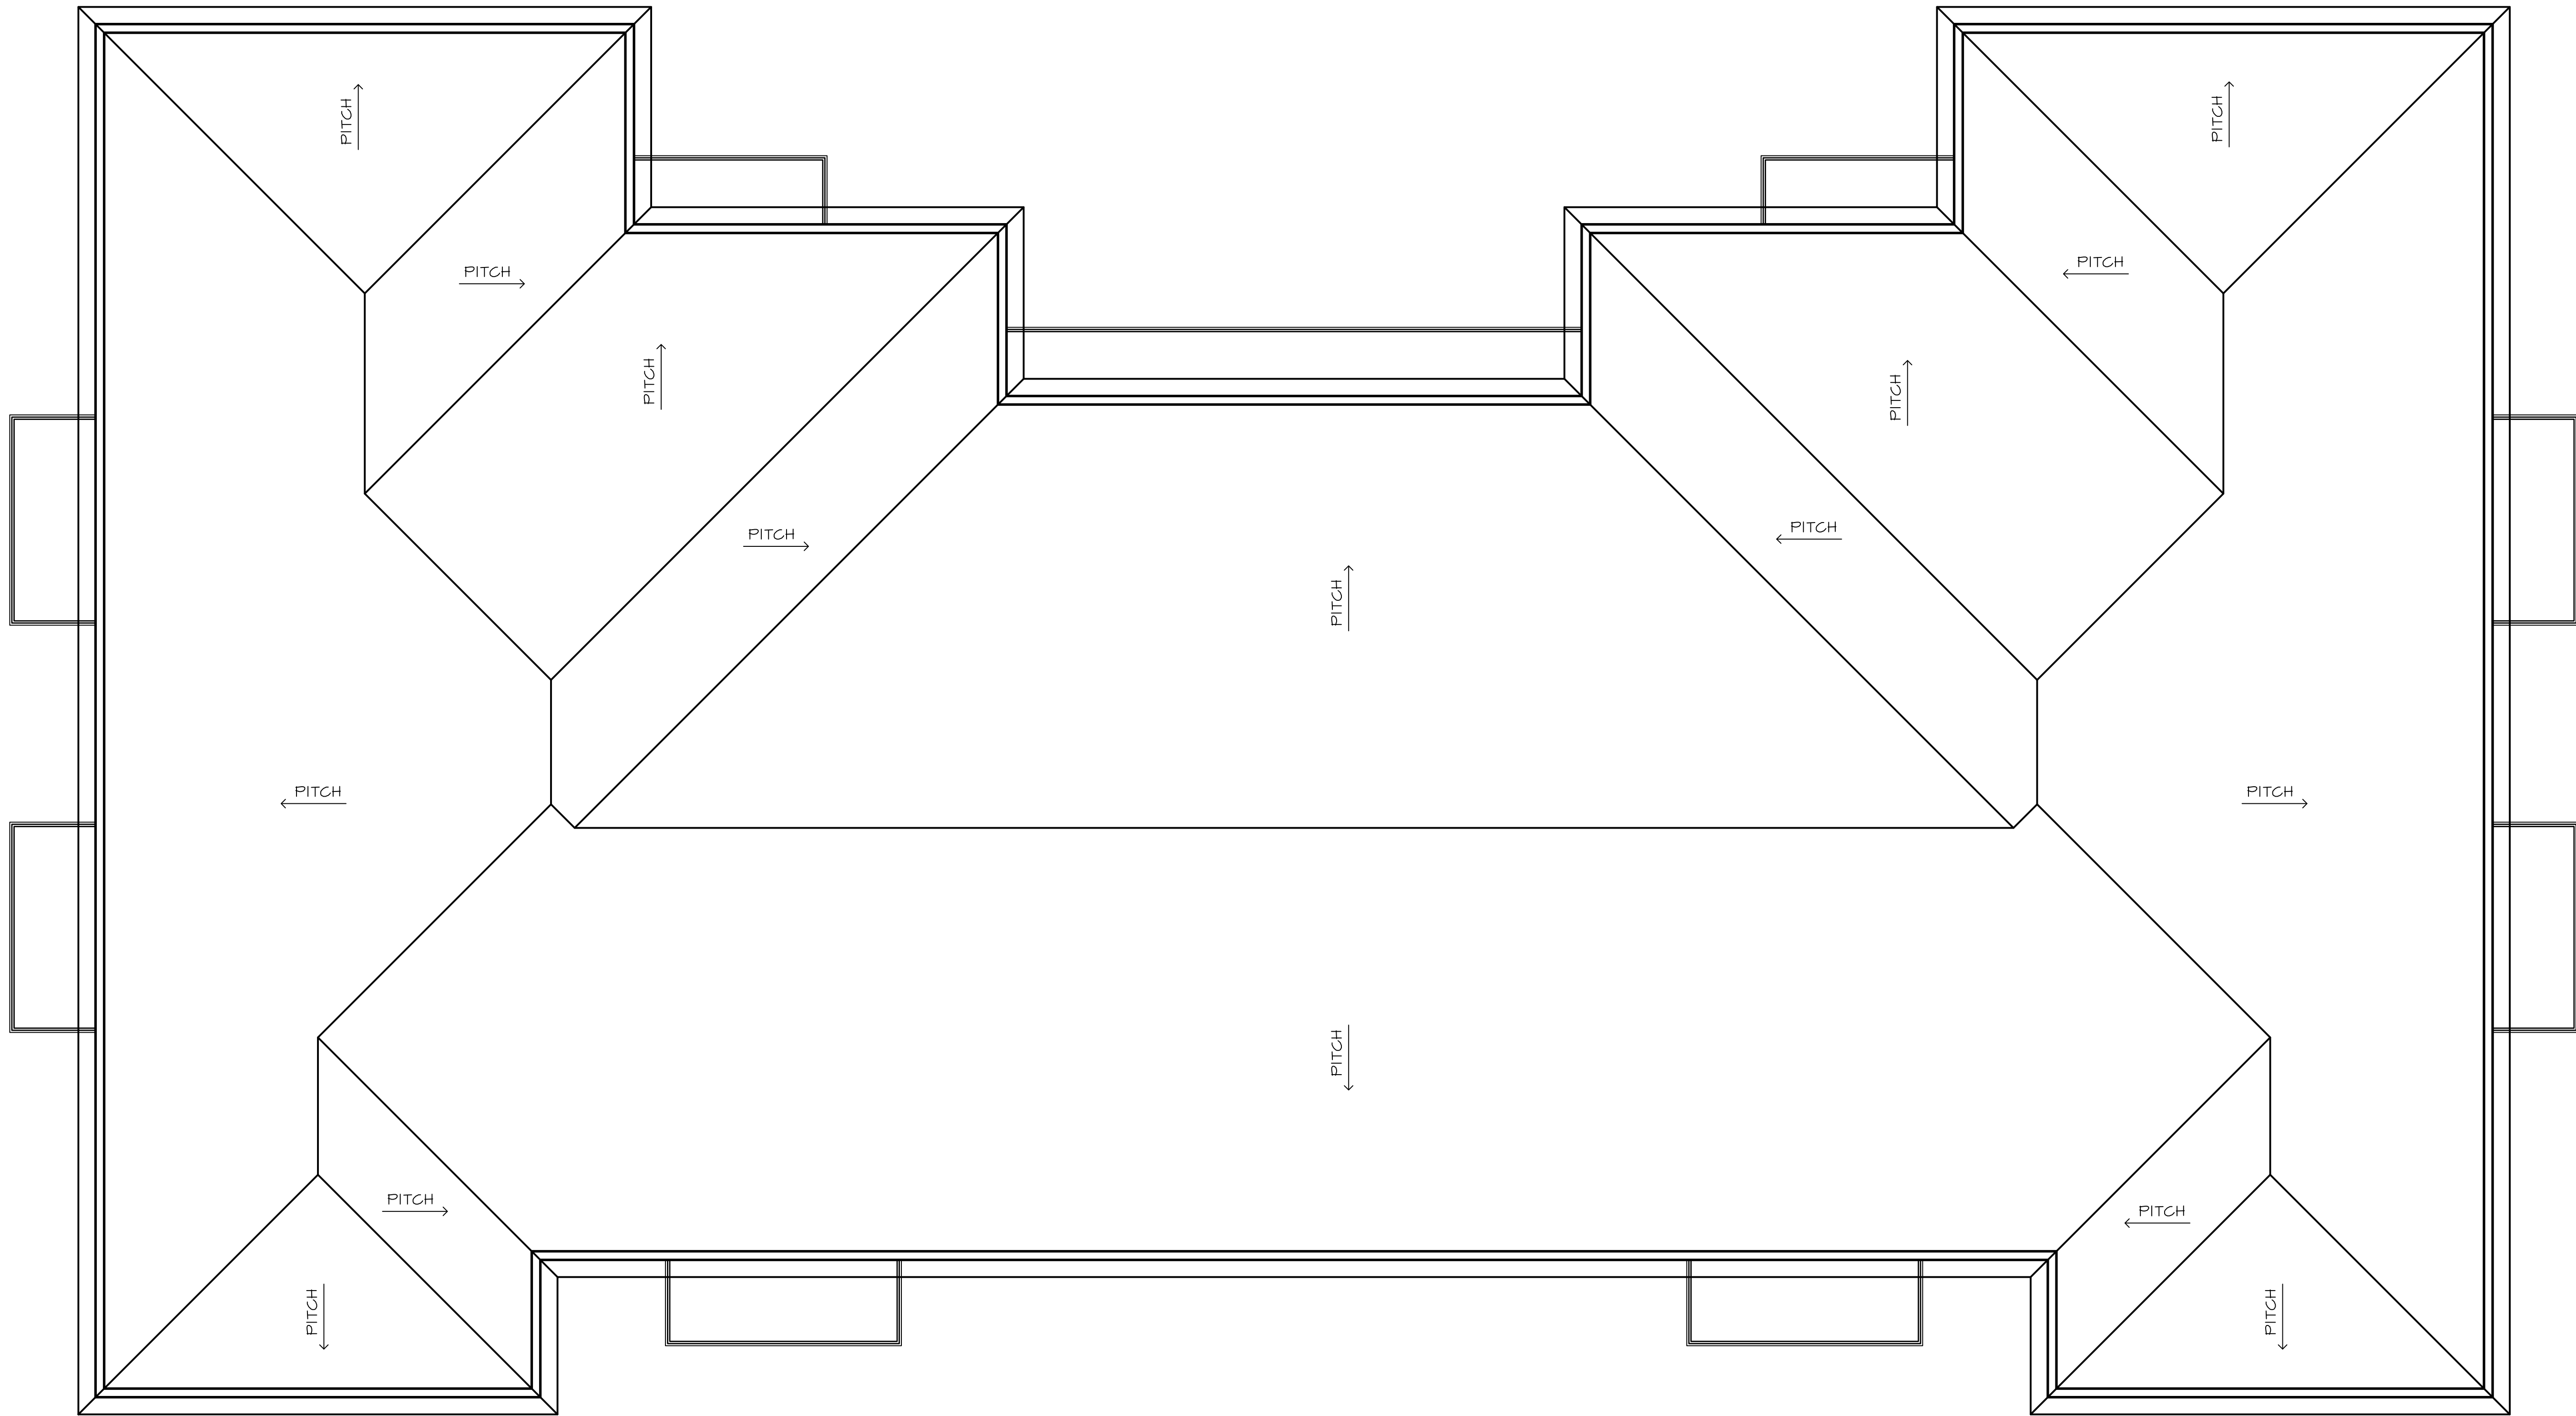

1 PROPOSED ROOF PLAN
3/16" = 1'-0"

Property:
COFFMAN APTS
INDIANAPOLIS, IN

Client:
COHEN MIZRACHI
PROPERTIES LLC

SEAL:

SCALE: AS NOTED

DWG BY: R.M.

Drawing Title:
PROPOSED
FLOOR PLANS

Drawing Number:

A-102.00

03 of 05



② PROPOSED SIDE (SOUTH) ELEVATION
3/16" = 1'-0"



① PROPOSED REAR (EAST) ELEVATION
3/16" = 1'-0"

Property:
COFFMAN APTS
INDIANAPOLIS, IN

Client:
COHEN MIZRACHI
PROPERTIES LLC

SEAL:

SCALE: AS NOTED

DWG BY: R.M.

Drawing Title:
PROPOSED
ELEVATIONS


Drawing Number:

A-201.00

05 of 05



② PROPOSED SIDE (NORTH) ELEVATION
3/16" = 1'-0"

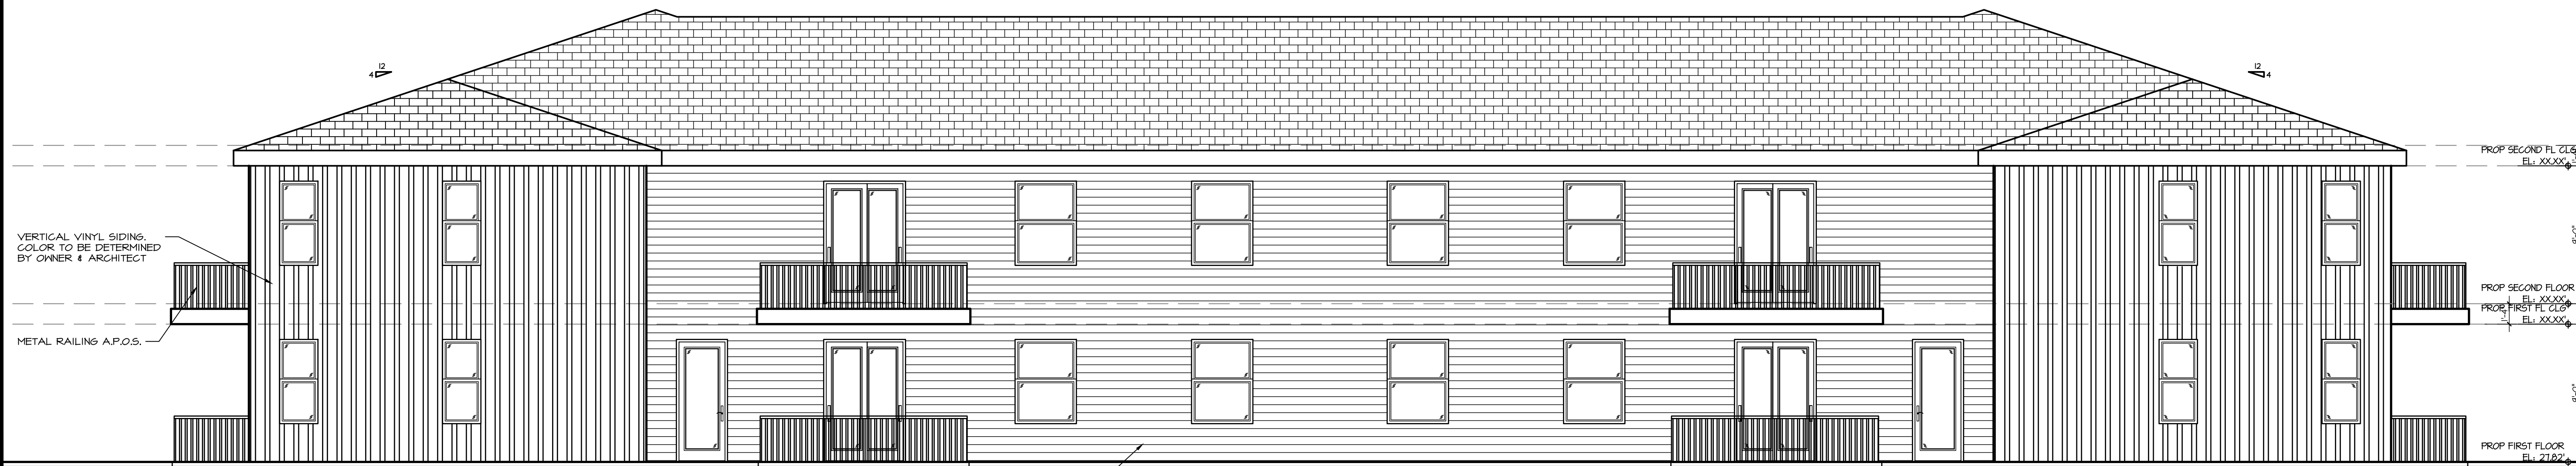

① PROPOSED FRONT (WEST) ELEVATION
3/16" = 1'-0"

Property:
COFFMAN APTS
INDIANAPOLIS, IN

Client:
**COHEN MIZRACHI
PROPERTIES LLC**

SEAL:

SCALE: AS NOTED

DWG BY: R.M.

Drawing Title:
**PROPOSED
ELEVATIONS**

Drawing Number:

A-200.00

04 of 05